

商業辦公室裝修工程

COMMERCIAL OFFICE FIT-OUT · SCHEDULE BASELINE REPORT

01 專案摘要

PROJECT SUMMARY

PROJECT NO.
LPM-2026-0417
專案編號

BASELINE
Baseline Rev. B
基準版本

DATA DATE
2026-09-04
資料日期

SHEET
A3 · 01 / 04
圖幅 / 頁

基準總工期
BASELINE DURATION

97

工作天 working days

開工日期
START

2026-10-05

Monday

實際完工
PRACTICAL COMPLETION

2027-01-29

Friday

任務 / 里程碑
TASKS / MILESTONES

38 / 5

8 個階段 phases

關鍵任務
CRITICAL TASKS

18

佔 47% · 近關鍵 3 項

P80 完工緩衝
P80 CONTINGENCY

+8

工作天 · P80 = 105 d · 準時機率 2%


1.1 階段摘要 PHASE SUMMARY

工作天 working days · 關鍵工期 = 階段內關鍵任務工期合計 (含並行)

#	階段 PHASE	開始 START	完成 FINISH	歷時 SPAN	任務 TASKS	關鍵 CRITICAL	關鍵工期 CRIT. DAYS	時間分佈 TIMELINE
01	前期準備與採購 Pre-construction & Procurement	2026-10-05	2026-12-14	60	10	4	26	
02	拆除及清場 Demolition & Strip-out	2026-11-05	2026-11-16	10	3	3	10	
03	機電一次配管 MEP 1st Fix	2026-11-17	2026-11-27	10	5	2	20	
04	間隔與天花 Partitions & Ceilings	2026-11-28	2026-12-18	18	4	3	26	
05	機電二次配管 MEP 2nd Fix	2026-12-19	2027-01-06	13	6	0	0	
06	裝飾工程 Finishes	2026-12-15	2027-01-07	18	4	1	8	
07	木作與傢俬 Joinery & Furniture	2026-12-31	2027-01-25	21	4	3	17	
08	測試調試、IAQ 及交付 T&C, IAQ Gate & Handover	2027-01-07	2027-01-29	20	7	2	8	
合計 Total		2026-10-05	2027-01-29	97	38	18	115	

1.4 階段時間軸 PHASE TIMELINE

關鍵 critical 一般 non-critical 里程碑 milestone

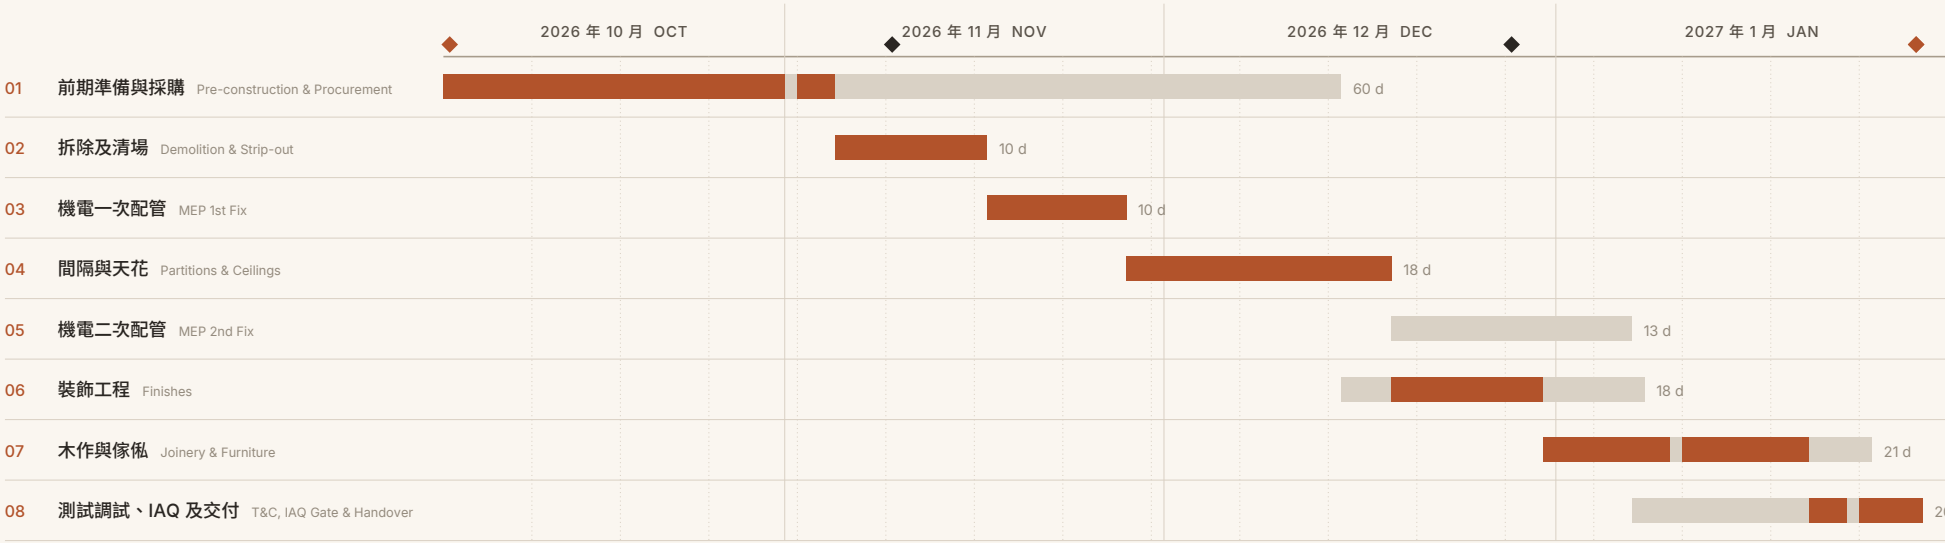

1.6 長交期採購決策點 LONG-LEAD PROCUREMENT · LATEST ORDER DATES

最遲開始 LS = 不影響完工日期的最後下單日

WBS	採購項目 ITEM	交期 LEAD TIME	計劃下單 PLANNED ORDER	最遲下單 LATEST ORDER (LS)	需到場日 REQUIRED ON SITE	浮時 FLOAT	後續工序 FEEDS
1.7	玻璃間隔及木作 Glass Partition & Joinery	30 d	2026-10-23	2026-11-05	2026-12-10	11 d	玻璃間隔安裝 · 固定木作安裝
1.8	活動傢俬 Loose Furniture	45 d	2026-10-23	2026-11-20	2027-01-15	24 d	活動傢俬進場及安裝
1.9	燈具及影音設備 Lighting & AV Equipment	25 d	2026-10-23	2026-12-10	2027-01-12	41 d	燈具及天花設備安裝

1.2 里程碑 MILESTONES

合約簽署及啟動會議 CONTRACT AWARD & KICK-OFF	2026-10-05 關鍵 critical
法定審批取得 STATUTORY APPROVALS OBTAINED	2026-11-09 浮時 float 8 d
天花封閉 CEILING CLOSE-UP	2026-12-28 浮時 float 17 d
實際完工及交付 PRACTICAL COMPLETION & HANDOVER	2027-01-29 關鍵 critical
客戶入伙 CLIENT MOVE-IN	2027-01-29 關鍵 critical

1.3 專案資料 PROJECT INFORMATION

客戶 CLIENT	Meridian Capital Partners
地點 SITE	中環甲級商廈 32 樓 · 淨面積約 1,000 平方米
採購模式 PROCUREMENT	Design & Build (D&B)
工作曆 CALENDAR	六天工作週 (週一至週六) · 扣除公眾假期
公眾假期 HOLIDAYS	8 天於工期內 within window
排程方法 METHOD	CPM · Kahn 拓撲排序 · 前推 / 後推計算

1.5 進度重點 EXECUTIVE NOTES

- 基準總工期 97 個工作天 (2026 年 10 月 5 日至 2027 年 1 月 29 日)，關鍵路徑共 18 項工作任務，主要驅動工序：業主及大廈管理處審批 → 進場動員及圍板 → 保護工程及拆除 → 廢料清運及地台修補 → 放線定位 → 空調風管及 VAV 箱 → 輕鋼架間牆及封板 → 天花龍骨及燈槽 → 批盪及油漆。
- 近關鍵任務 (總浮時 ≤ 3 天) 共 3 項：消防噴淋改位、弱電及數據線槽、缺陷檢查及修正；任何一項延誤即可能改寫關鍵路徑。
- 長交期採購浮時：玻璃間隔及木作 11 天、活動傢俬 24 天、燈具及影音設備 41 天；所有長交期訂單須於 2026 年 10 月 23 日 前落實，否則玻璃間隔將成為關鍵。
- 蒙地卡羅模擬 (5,000 次) P50 = 102 天、P80 = 105 天，基準準時機率僅 2%；建議預留 8 個工作天工期緩衝。
- 最高風險：R01 消防法定申報審批延誤 (分數 20)，關聯任務最小浮時 8 天，延誤逾此浮時將直接推遲後續機電及間隔工序。

商業辦公室裝修工程

COMMERCIAL OFFICE FIT-OUT · SCHEDULE BASELINE REPORT

02 甘特圖


GANTT CHART · CPM BASELINE

PROJECT NO.
LPM-2026-0417
專案編號

BASELINE
Baseline Rev. B
基準版本

DATA DATE
2026-09-04
資料日期

SHEET
A3 · 02 / 04
圖幅 / 頁

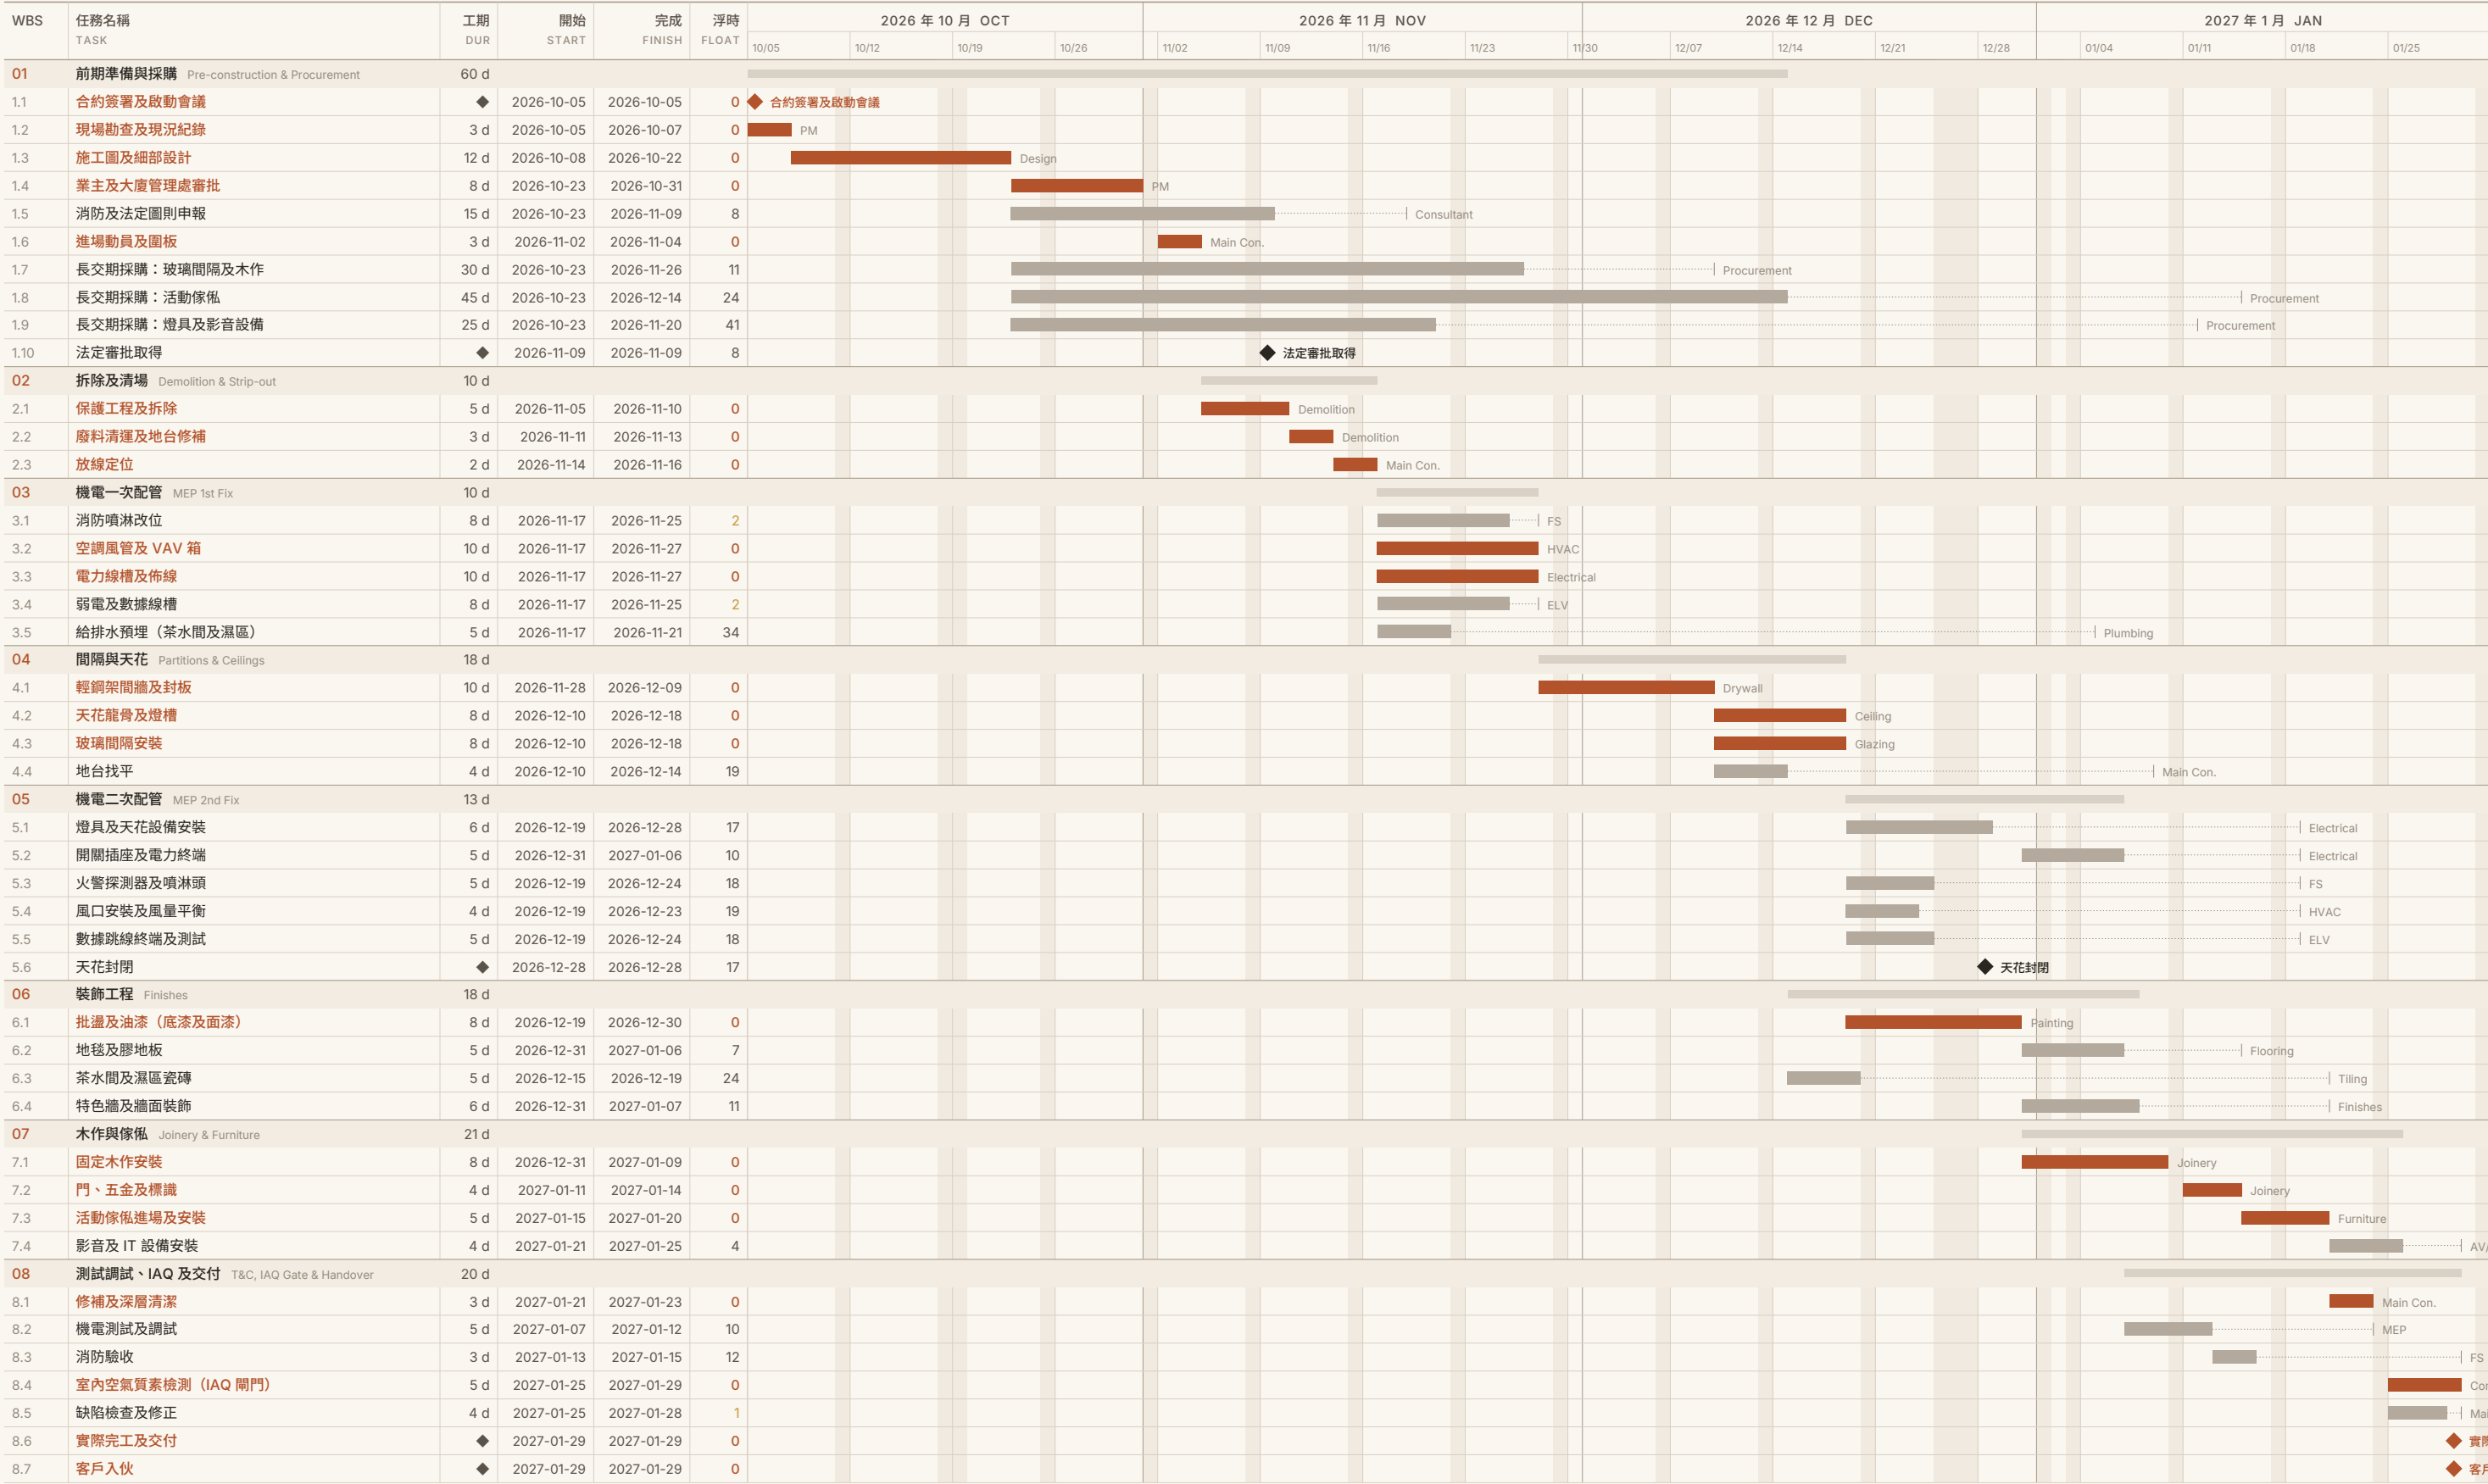

38 項任務 tasks · 5 個里程碑 milestones · 8 個階段 phases

關鍵任務 Critical (TF = 0)

一般任務 Non-critical

里程碑 Milestone

總浮時 Total float → 最遲完成 LF

非工作日 Non-working day

時間軸 2026-10-05 – 2027-01-31 · 17 週 weeks · 工作曆 Mon-Sat

商業辦公室裝修工程

COMMERCIAL OFFICE FIT-OUT · SCHEDULE BASELINE REPORT

03 關鍵路徑

CRITICAL PATH ANALYSIS

PROJECT NO.
LPM-2026-0417
專案編號

BASELINE
Baseline Rev. B
基準版本

DATA DATE
2026-09-04
資料日期

SHEET
A3 · 03 / 04
圖幅 / 頁

3.1 關鍵鏈

19 個節點 nodes · 總浮時 TF = 0 · 97 工作天



3.2 關鍵任務明細

CRITICAL TASKS · CPM METRICS

ES / EF / LS / LF 以工作天偏移表示 · CI = 蒙地卡羅關鍵度指數

WBS	任務 TASK	工種 TRADE	工期 DUR	ES	EF	LS	LF	TF	開始 START	完成 FINISH	CI	
1.1	合約簽署及啟動會議	PM	◆	0	0	0	0	0	2026-10-05	2026-10-05	100%	
1.2	現場勘查及現況紀錄	PM	3	0	3	0	3	0	2026-10-05	2026-10-07	100%	
1.3	施工圖及細部設計	Design	12	3	15	3	15	0	2026-10-08	2026-10-22	100%	
1.4	業主及大廈管理處審批	PM	8	15	23	15	23	0	2026-10-23	2026-10-31	99%	
1.6	進場動員及圍板	Main Con.	3	23	26	23	26	0	2026-11-02	2026-11-04	99%	
2.1	保護工程及拆除	Demolition	5	26	31	26	31	0	2026-11-05	2026-11-10	99%	
2.2	廢料清運及地台修補	Demolition	3	31	34	31	34	0	2026-11-11	2026-11-13	99%	
2.3	放線定位	Main Con.	2	34	36	34	36	0	2026-11-14	2026-11-16	99%	
3.2	空調風管及 VAV 箱	HVAC	10	36	46	36	46	0	2026-11-17	2026-11-27	31%	
3.3	電力線槽及佈線	Electrical	10	36	46	36	46	0	2026-11-17	2026-11-27	54%	
4.1	輕鋼架間牆及封板	Drywall	10	46	56	46	56	0	2026-11-28	2026-12-09	100%	
4.2	天花龍骨及燈槽	Ceiling	8	56	64	56	64	0	2026-12-10	2026-12-18	50%	
4.3	玻璃間隔安裝	Glazing	8	56	64	56	64	0	2026-12-10	2026-12-18	50%	
6.1	批盪及油漆 (底漆及面漆)	Painting	8	64	72	64	72	0	2026-12-19	2026-12-30	100%	
7.1	固定木作安裝	Joinery	8	72	80	72	80	0	2026-12-31	2027-01-09	100%	
7.2	門、五金及標識	Joinery	4	80	84	80	84	0	2027-01-11	2027-01-14	100%	
7.3	活動傢俬進場及安裝	Furniture	5	84	89	84	89	0	2027-01-15	2027-01-20	100%	
8.1	修補及深層清潔	Main Con.	3	89	92	89	92	0	2027-01-21	2027-01-23	100%	
8.4	室內空氣質素檢測 (IAQ 關門)	Consultant	5	92	97	92	97	0	2027-01-25	2027-01-29	100%	
8.6	實際完工及交付	PM	◆	97	97	97	97	0	2027-01-29	2027-01-29	100%	
8.7	客戶入伙	Client	◆	97	97	97	97	0	2027-01-29	2027-01-29	100%	

3.5 路徑驅動因素

PATH DRIVERS

- 01

前期準備佔關鍵路徑 26 個工作天 (27%)：設計及業主審批直接決定進場日期，每延誤一天即等量推遲完工。
- 02

機電一次配管以 空調風管及 VAV 箱 為主導；消防噴淋改位及弱電線槽僅有 2 天浮時，停水窗口一旦受限即會取代其成為關鍵。
- 03

匯合節點 (merge bias)：輕鋼架間牆及封板 (4 項前置)、活動傢俬進場及安裝 (3 項前置)、修補及深層清潔 (3 項前置)。多項前置工序同時匯入，令模擬完工分佈明顯偏後。
- 04

完工前工序 (修補清潔 → IAQ 檢測) 為串行硬性關門，無法壓縮；缺陷修正僅 1 天浮時。

3.3 近關鍵任務


NEAR-CRITICAL · TF ≤ 7 D

WBS	任務 TASK	工期 DUR	總浮時 TF	自由浮時 FF	浮時對比 FLOAT	CI
3.1	消防噴淋改位	8	2	2		15%
3.4	弱電及數據線槽	8	2	2		0%
6.2	地毯及膠地板	5	7	7		0%
7.4	影音及 IT 設備安裝	4	4	4		0%
8.5	缺陷檢查及修正	4	1	1		0%

3.4 關鍵工期構成

CRITICAL DURATION BY PHASE


合計 115 工作天

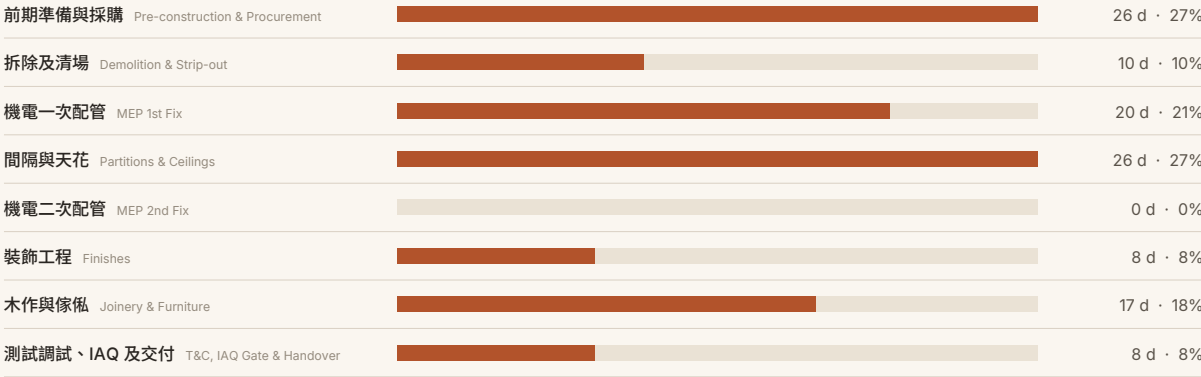

3.6 關鍵度指數

CRITICALITY INDEX · NON-CRITICAL TASKS


5,000 次蒙地卡羅 runs

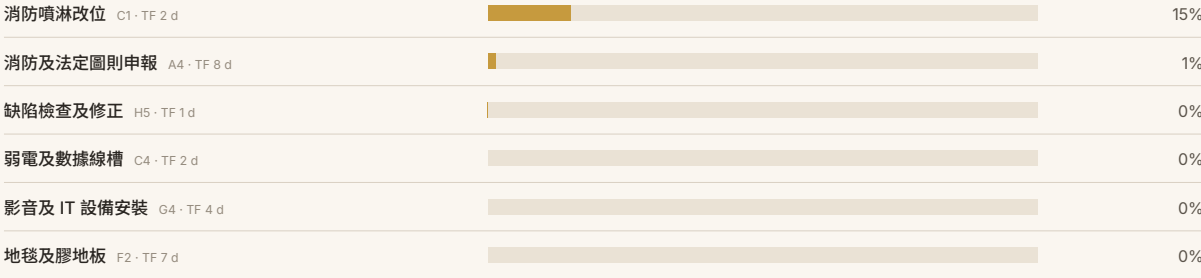

關鍵度指數 CI = 該任務在 5,000 次模擬中落於關鍵路徑的比例。消防噴淋改位 雖有 2 天浮時，仍有 15% 機率成為關鍵，應納入每週關鍵路徑監控。


4.1 風險矩陣 PROBABILITY × IMPACT MATRIX

12 項風險 risks

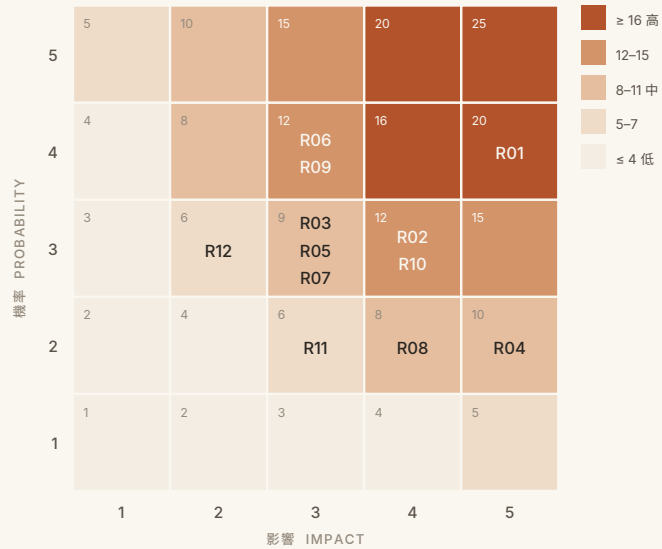


4.2 完工機率曲線 COMPLETION PROBABILITY · S-CURVE

5,000 次蒙地卡羅 runs

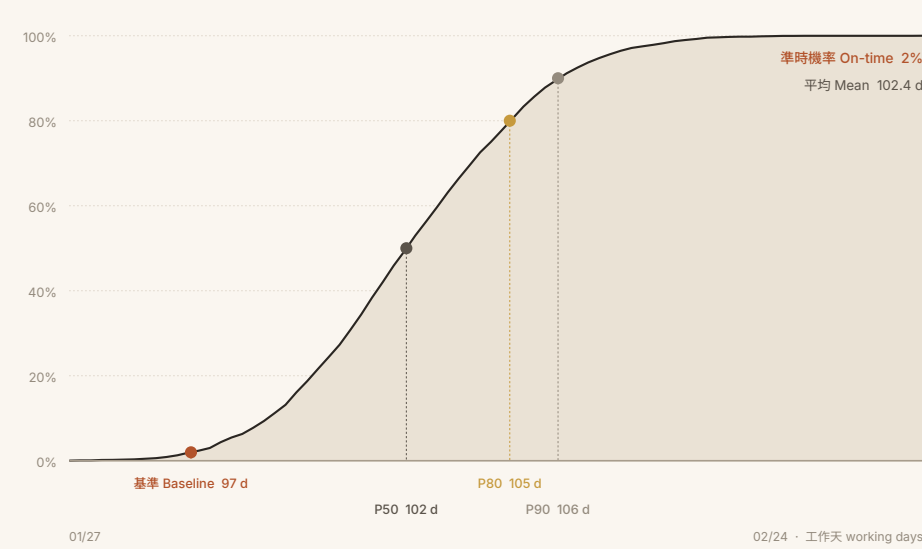

4.3 浮時分佈 TOTAL FLOAT DISTRIBUTION

38 項工作任務 tasks

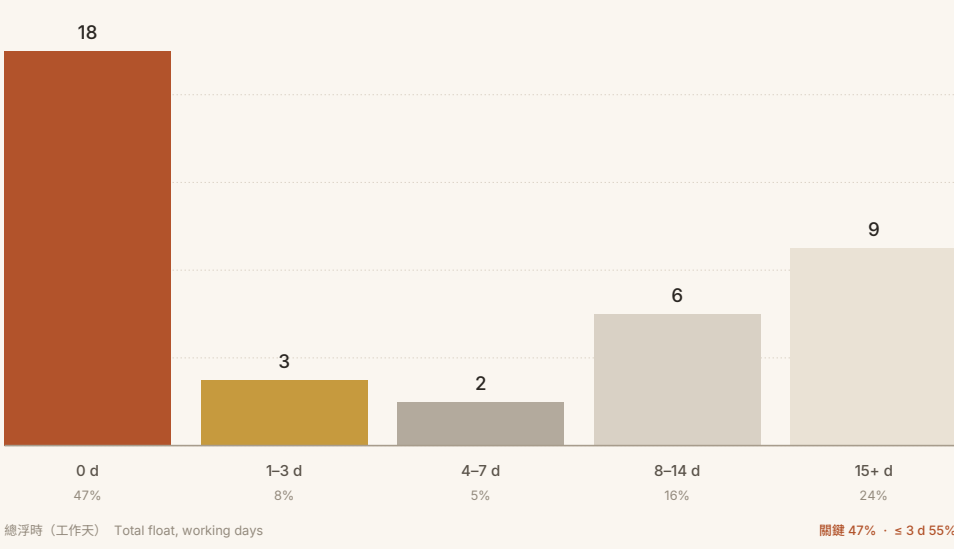

4.4 進度風險登記冊 SCHEDULE RISK REGISTER

P 機率 1-5 · I 影響 1-5 · 預期延誤 = 延誤天數 × P / 5 · 傳導延誤 = max(0, 延誤 - 最小浮時)

編號 ID	風險描述 RISK	DESCRIPTION	關聯任務 LINKED TASKS	階段 PHASE	P	I	分數 SCORE	等級 LEVEL	最小浮時 MIN FLOAT	延誤天數 DELAY	預期延誤 EXPECTED	傳導延誤 TO FINISH	應對措施 RESPONSE	負責 OWNER
R01	消防法定申報審批延誤	Statutory fire submission approval delay	1.5	01	4	5	20	高 high	8 d	10 d	8.0 d	2 d	提前預審；準備替代噴淋方案；預留審批浮時	Consultant
R09	裝飾階段客戶變更要求	Client change requests during finishes	6.4 · 7.1	06 · 07	4	3	12	中 medium	0 d	6 d	4.8 d	6 d	設計凍結日期；變更影響評估流程	PM
R06	噴淋停水窗口受大廈限制	Sprinkler shutdown windows restricted	3.1	03	4	3	12	中 medium	2 d	4 d	3.2 d	2 d	預訂夜間及週末停水時段；分區施工	FS
R02	玻璃間隔及木作進口船期延誤	Glass partition / joinery shipment delay	1.7	01	3	4	12	中 medium	11 d	7 d	4.2 d	—	下單前鎖定船期；分批出貨；本地備選供應商	Procurement
R10	消防驗收改期	Fire Services inspection rescheduled	8.3	08	3	4	12	中 medium	12 d	5 d	3.0 d	—	提前 3 週預約；預驗收自檢	FS
R04	拆除時發現隱蔽狀況（石棉／結構）	Hidden conditions found during strip-out	2.1	02	2	5	10	中 medium	0 d	8 d	3.2 d	8 d	開工前局部開孔勘查；備用檢測承辦商	Main Con.
R03	活動傢俬清關延誤	Loose furniture customs clearance delay	1.8 · 7.3	01 · 07	3	3	9	中 medium	0 d	5 d	3.0 d	5 d	提早 2 週下單；預先報關；臨時傢俬方案	Procurement
R05	業主審批要求修改設計	Landlord approval requires design revision	1.4	01	3	3	9	中 medium	0 d	5 d	3.0 d	5 d	早期與管理處預審；同步提交多方案	PM
R07	機電二次配管工序擠壓、人手不足	Trade congestion / labour shortage at 2nd fix	5.1 · 5.2	05	3	3	9	中 medium	10 d	4 d	2.4 d	—	分區交接計劃；提前鎖定分判人手	MEP
R08	IAQ 檢測不合格需沖洗	IAQ test failure requiring flush-out	8.4	08	2	4	8	中 medium	0 d	5 d	2.0 d	5 d	選用低 VOC 材料；完工前 72 小時通風沖洗	Consultant
R12	貨梯及吊運預約受限	Goods lift / hoist booking constraints	2.2 · 7.3	02 · 07	3	2	6	低 low	0 d	2 d	1.2 d	2 d	每週預訂貨梯時段；夜間送貨	Main Con.
R11	主電掣接駁停電安排	Power shutdown for main switch tie-in	3.3	03	2	3	6	低 low	0 d	2 d	0.8 d	2 d	與管理處協調夜間停電；備用發電機	Electrical

4.5 各階段預期延誤曝險 EXPECTED DELAY EXPOSURE BY PHASE

工作天 working days · 機率加權 probability-weighted

前期準備與採購 Pre-construction & Procurement	16.7 d
拆除及清場 Demolition & Strip-out	3.8 d
機電一次配管 MEP 1st Fix	4.0 d
間隔與天花 Partitions & Ceilings	0.0 d
機電二次配管 MEP 2nd Fix	2.4 d
裝飾工程 Finishes	2.4 d
木作與傢俬 Joinery & Furniture	4.5 d
測試調試、IAQ 及交付 T&C, IAQ Gate & Handover	5.0 d

4.6 工期緩衝建議 CONTINGENCY RECOMMENDATION

基準完工 BASELINE FINISH 2027-01-29 97 工作天 · 準時機率 2%	P50 完工 P50 FINISH 2027-02-04 102 工作天 · +5 d	P80 完工（建議承諾） P80 FINISH · RECOMMENDED 2027-02-11 105 工作天 · 緩衝 +8 d
---	--	---

建議以 P80 作為對外承諾完工日期，並將 8 個工作天緩衝置於 IAQ 閘門之前；前期審批（R01）與長交期採購（R02 / R03）為緩衝消耗的主要來源，須每週檢視浮時消耗。